



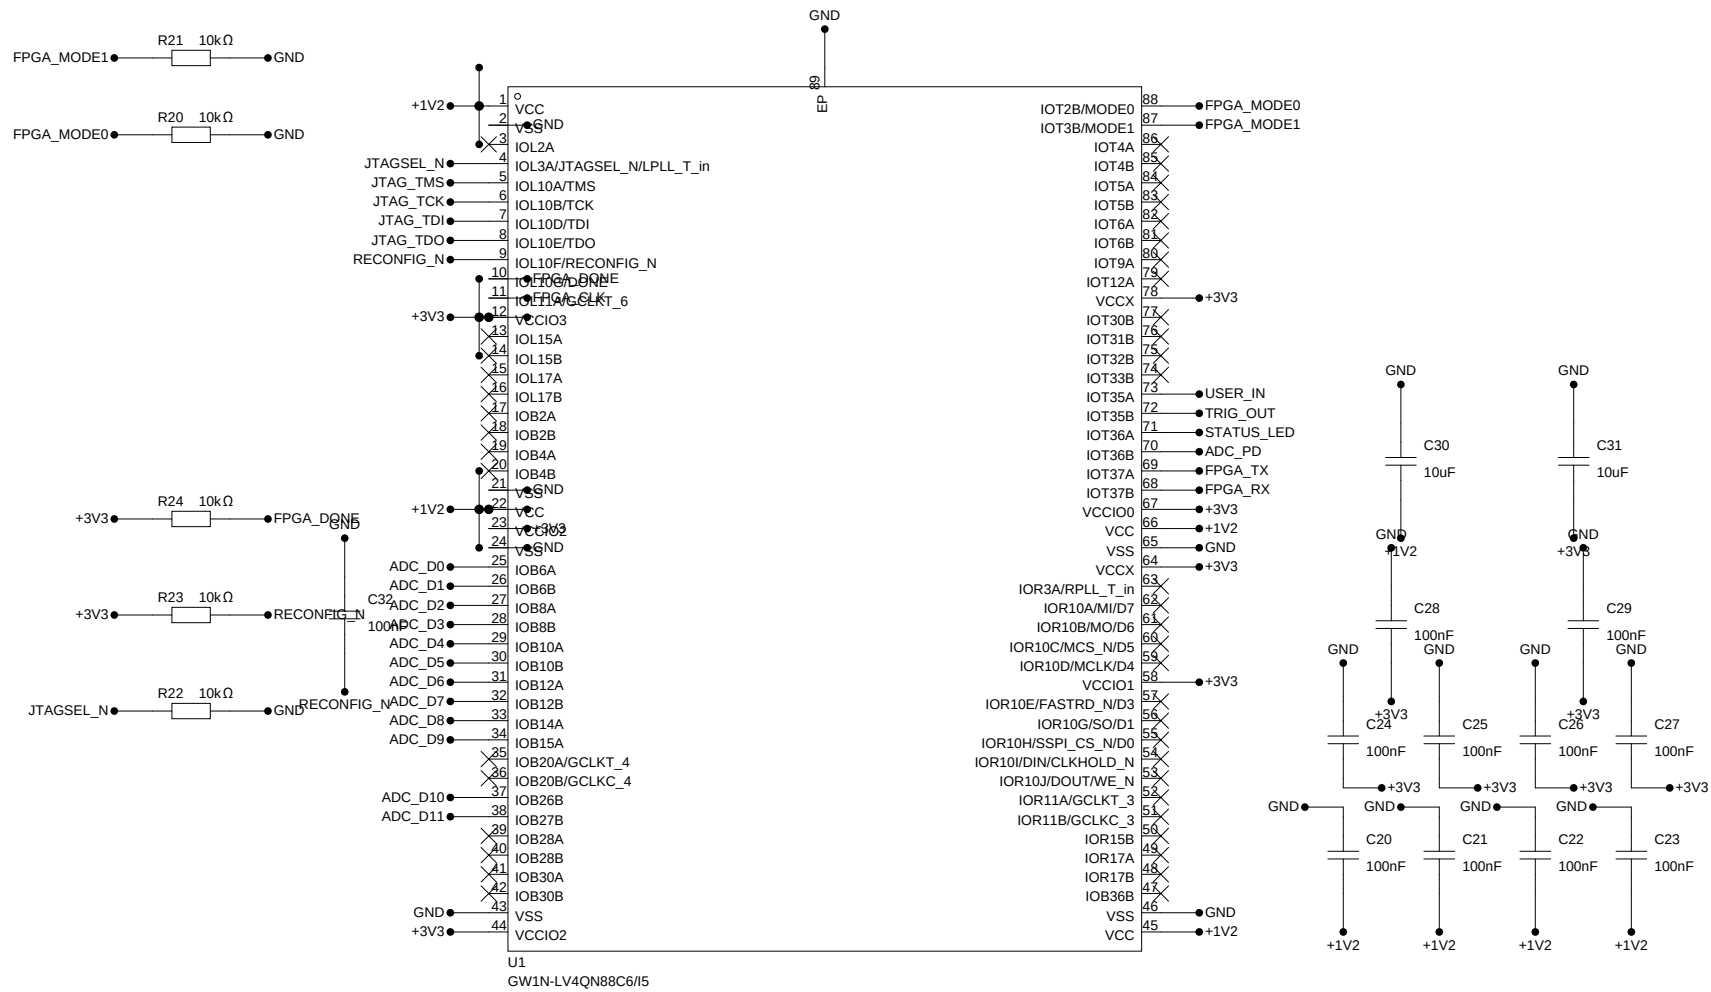





10 MSPS capture; falling-edge latch. JTAGSEL_N and MODE[1:0] are held low for recovery/autoboot.

GW1N-LV4QN88 | 4096 x 32-bit histogram + 1024 x 12-bit waveform window

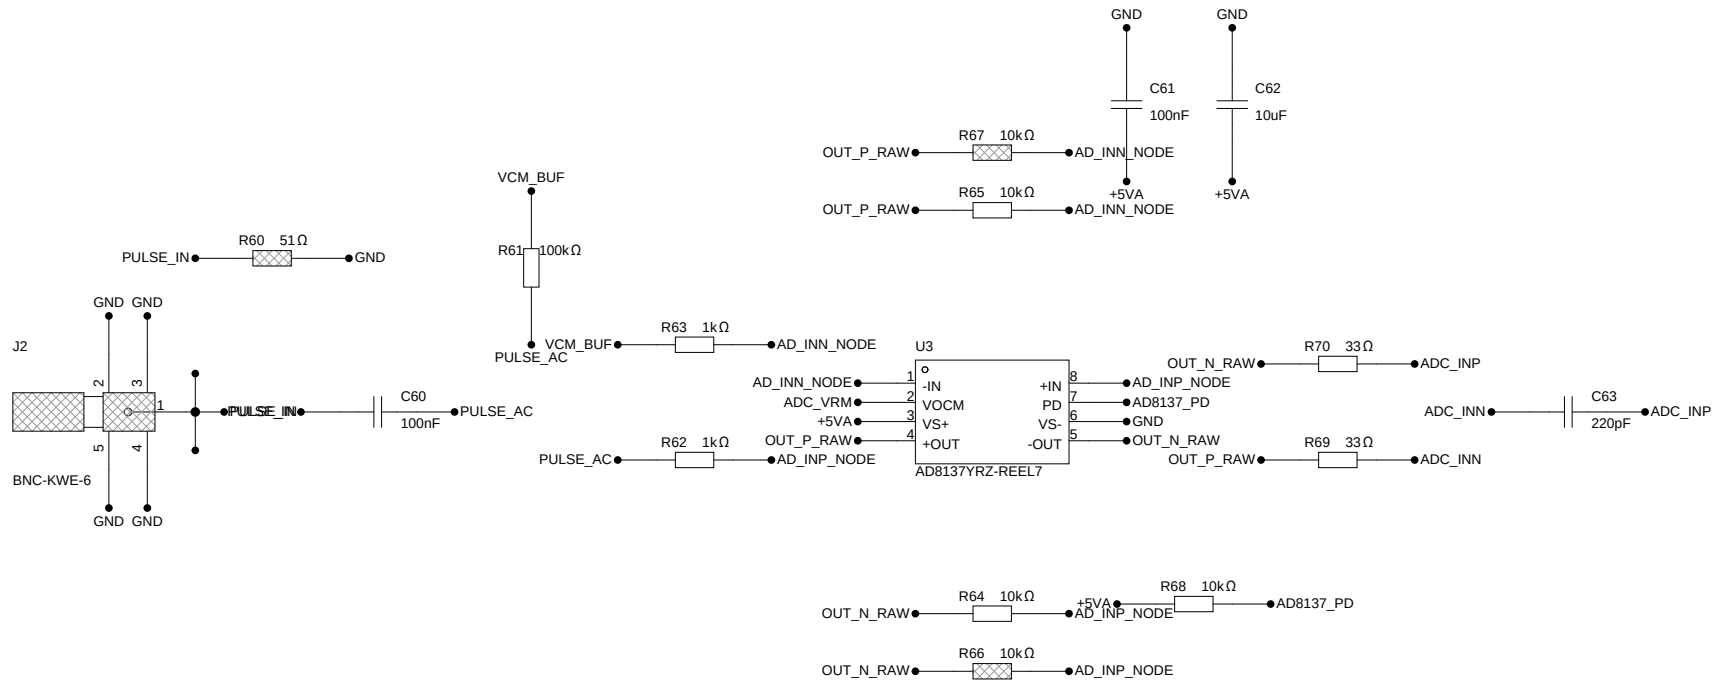

For the measured negative PMT pulses. FPGA polarity is selectable; this BNC must never carry detector high voltage.

Low-voltage pulse input | AC coupled | default gain x10 | 51 ohm termination optional

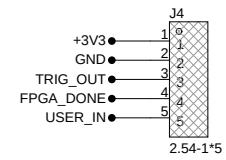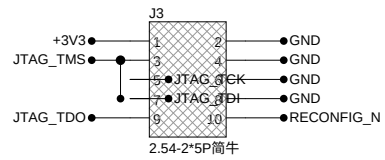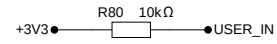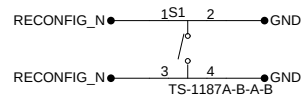

J3 is the fall-back JTAG connector; normal programming and data use the USB-C connector.

Rescue / test access | headers are DNP by default